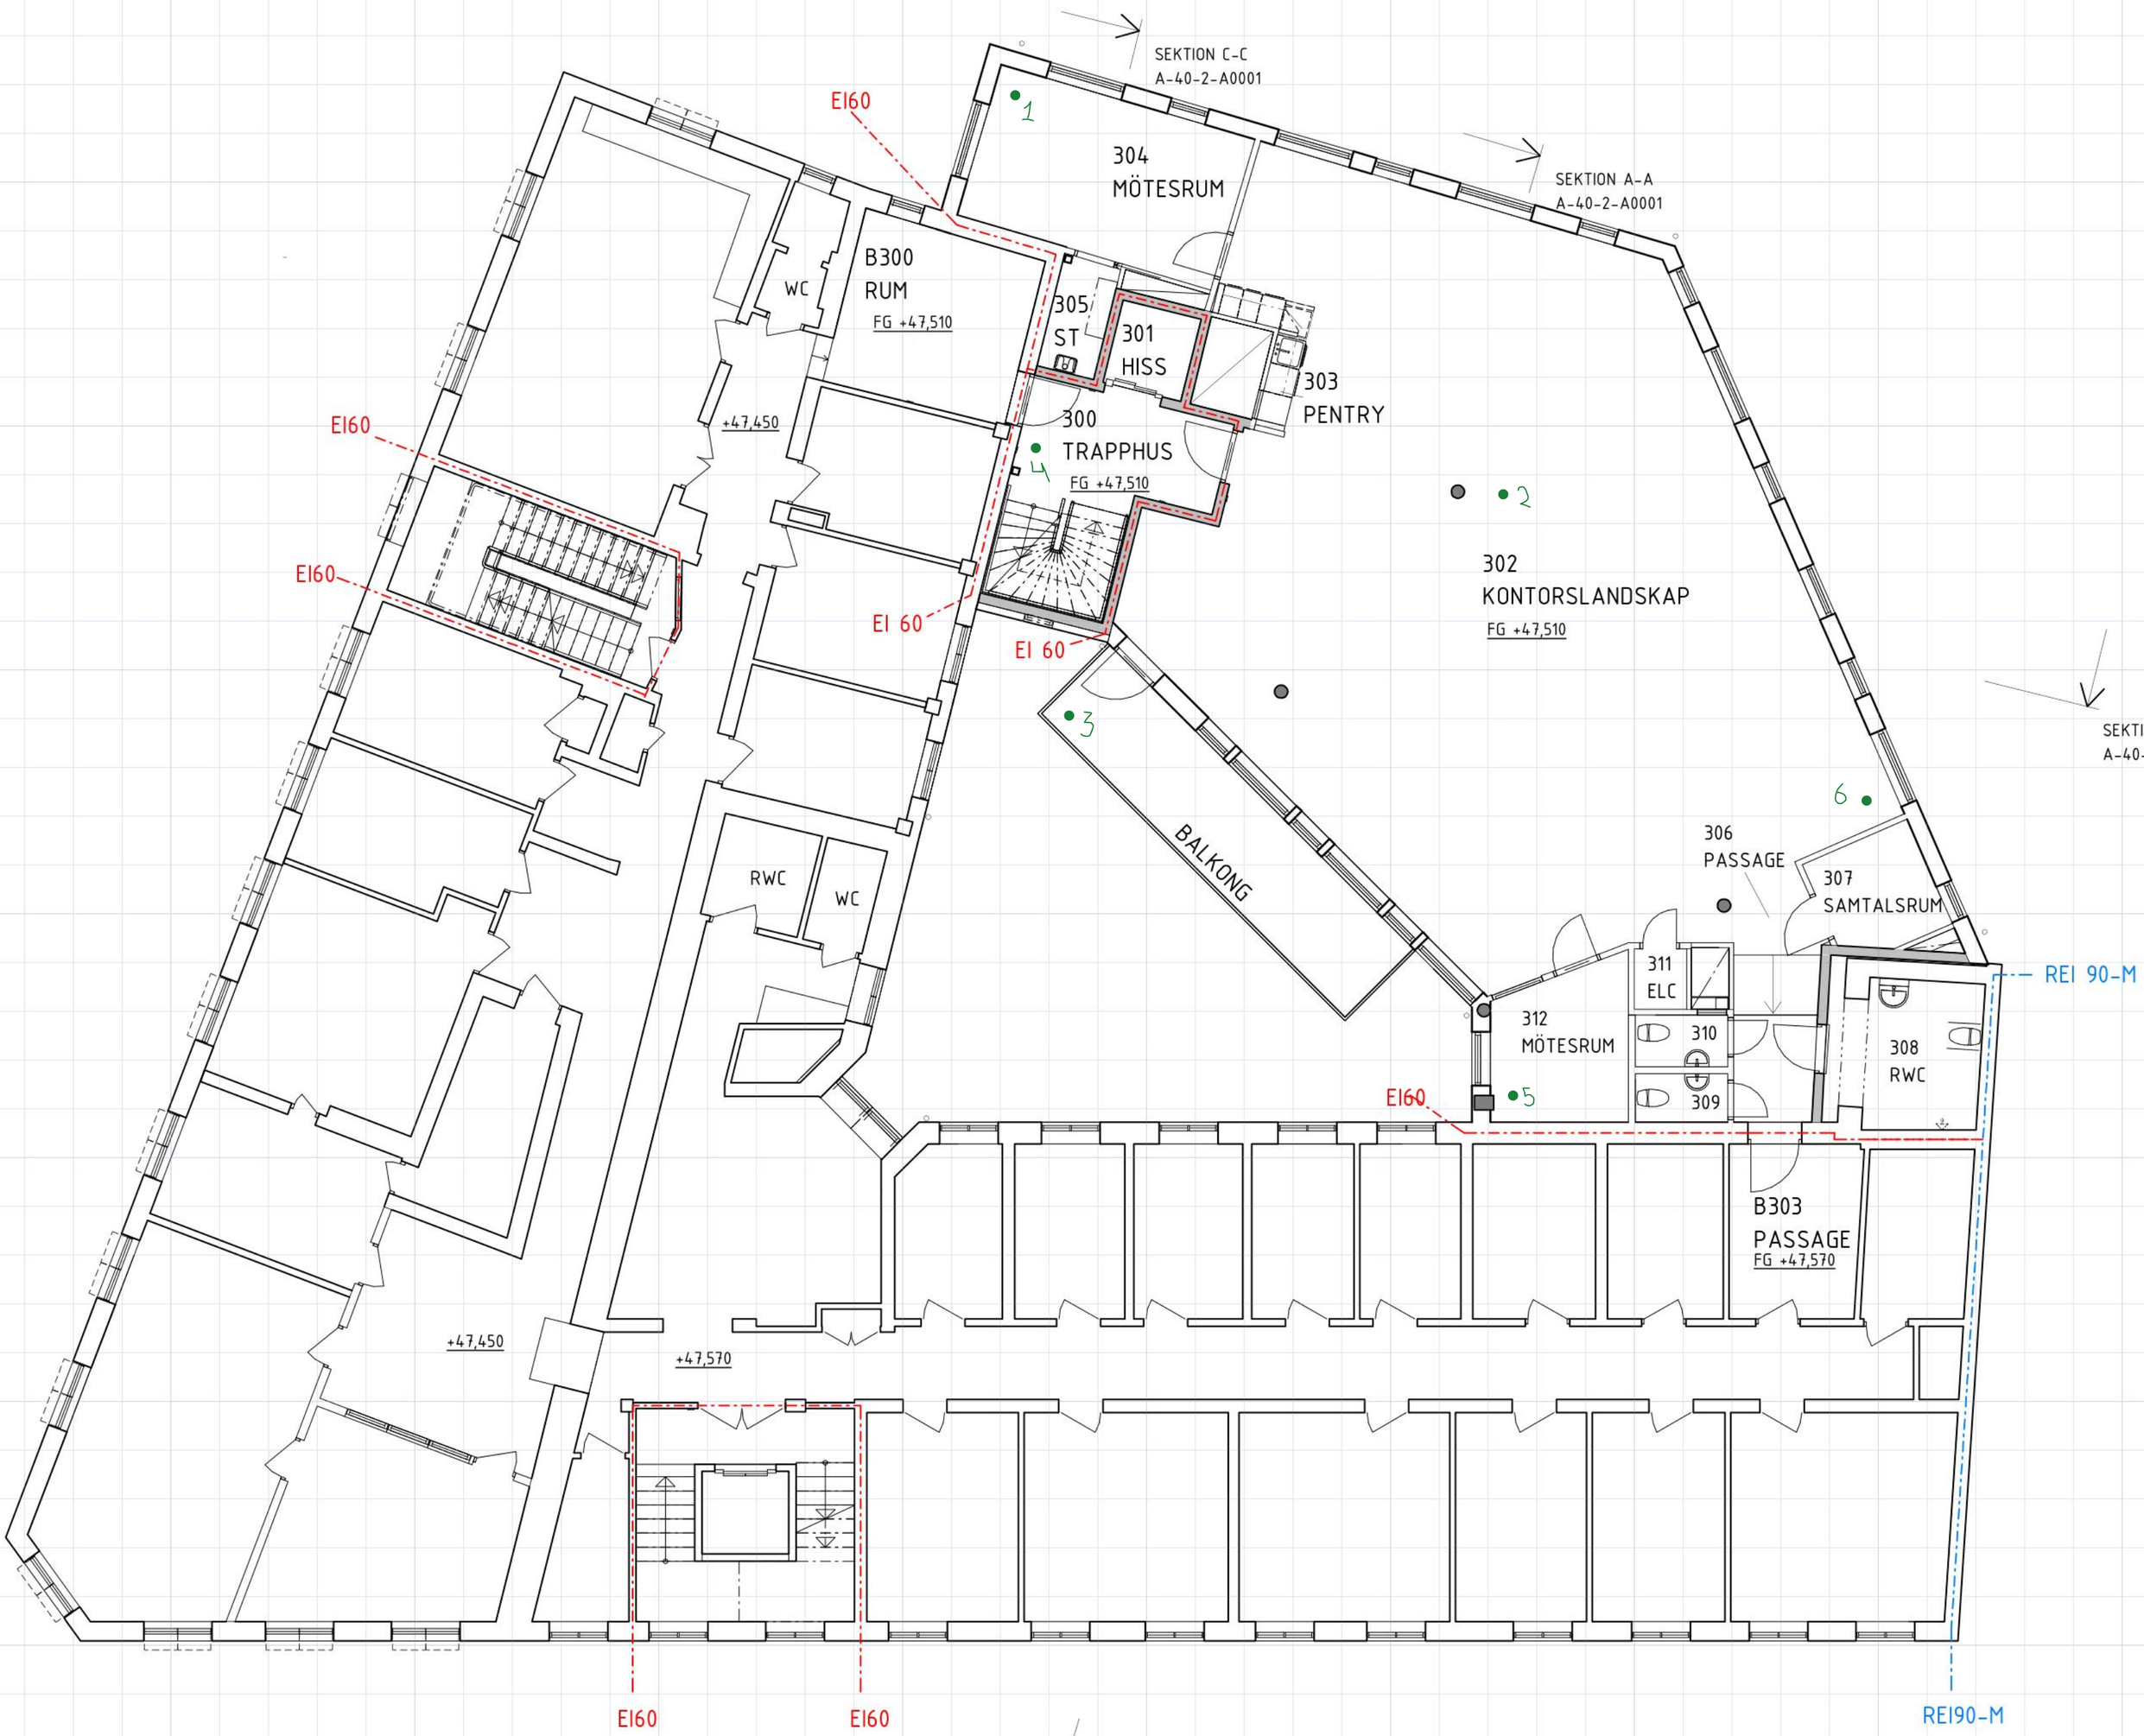
SEKTION C-C
A-40-2-A0001
SEKTION A-A
A-40-2-A0001
EI60
304
MÖTESRUM
B300
RUM
FG +47,510
WC
305
ST
301
HISS
303
PENTRY
300
TRAPPHUS
FG +47,510
+47,450
EI60
EI60
EI 60
EI 60
302
KONTORSLANDSKAP
FG +47,510
BALKONG
RWC
WC
306
PASSAGE
307
SAMTALSRUM
311
ELC
310
309
312
MÖTESRUM
308
RWC
REI 90-M
EI60
B303
PASSAGE
FG +47,570
+47,450
+47,570
EI60
EI60
REI90-M