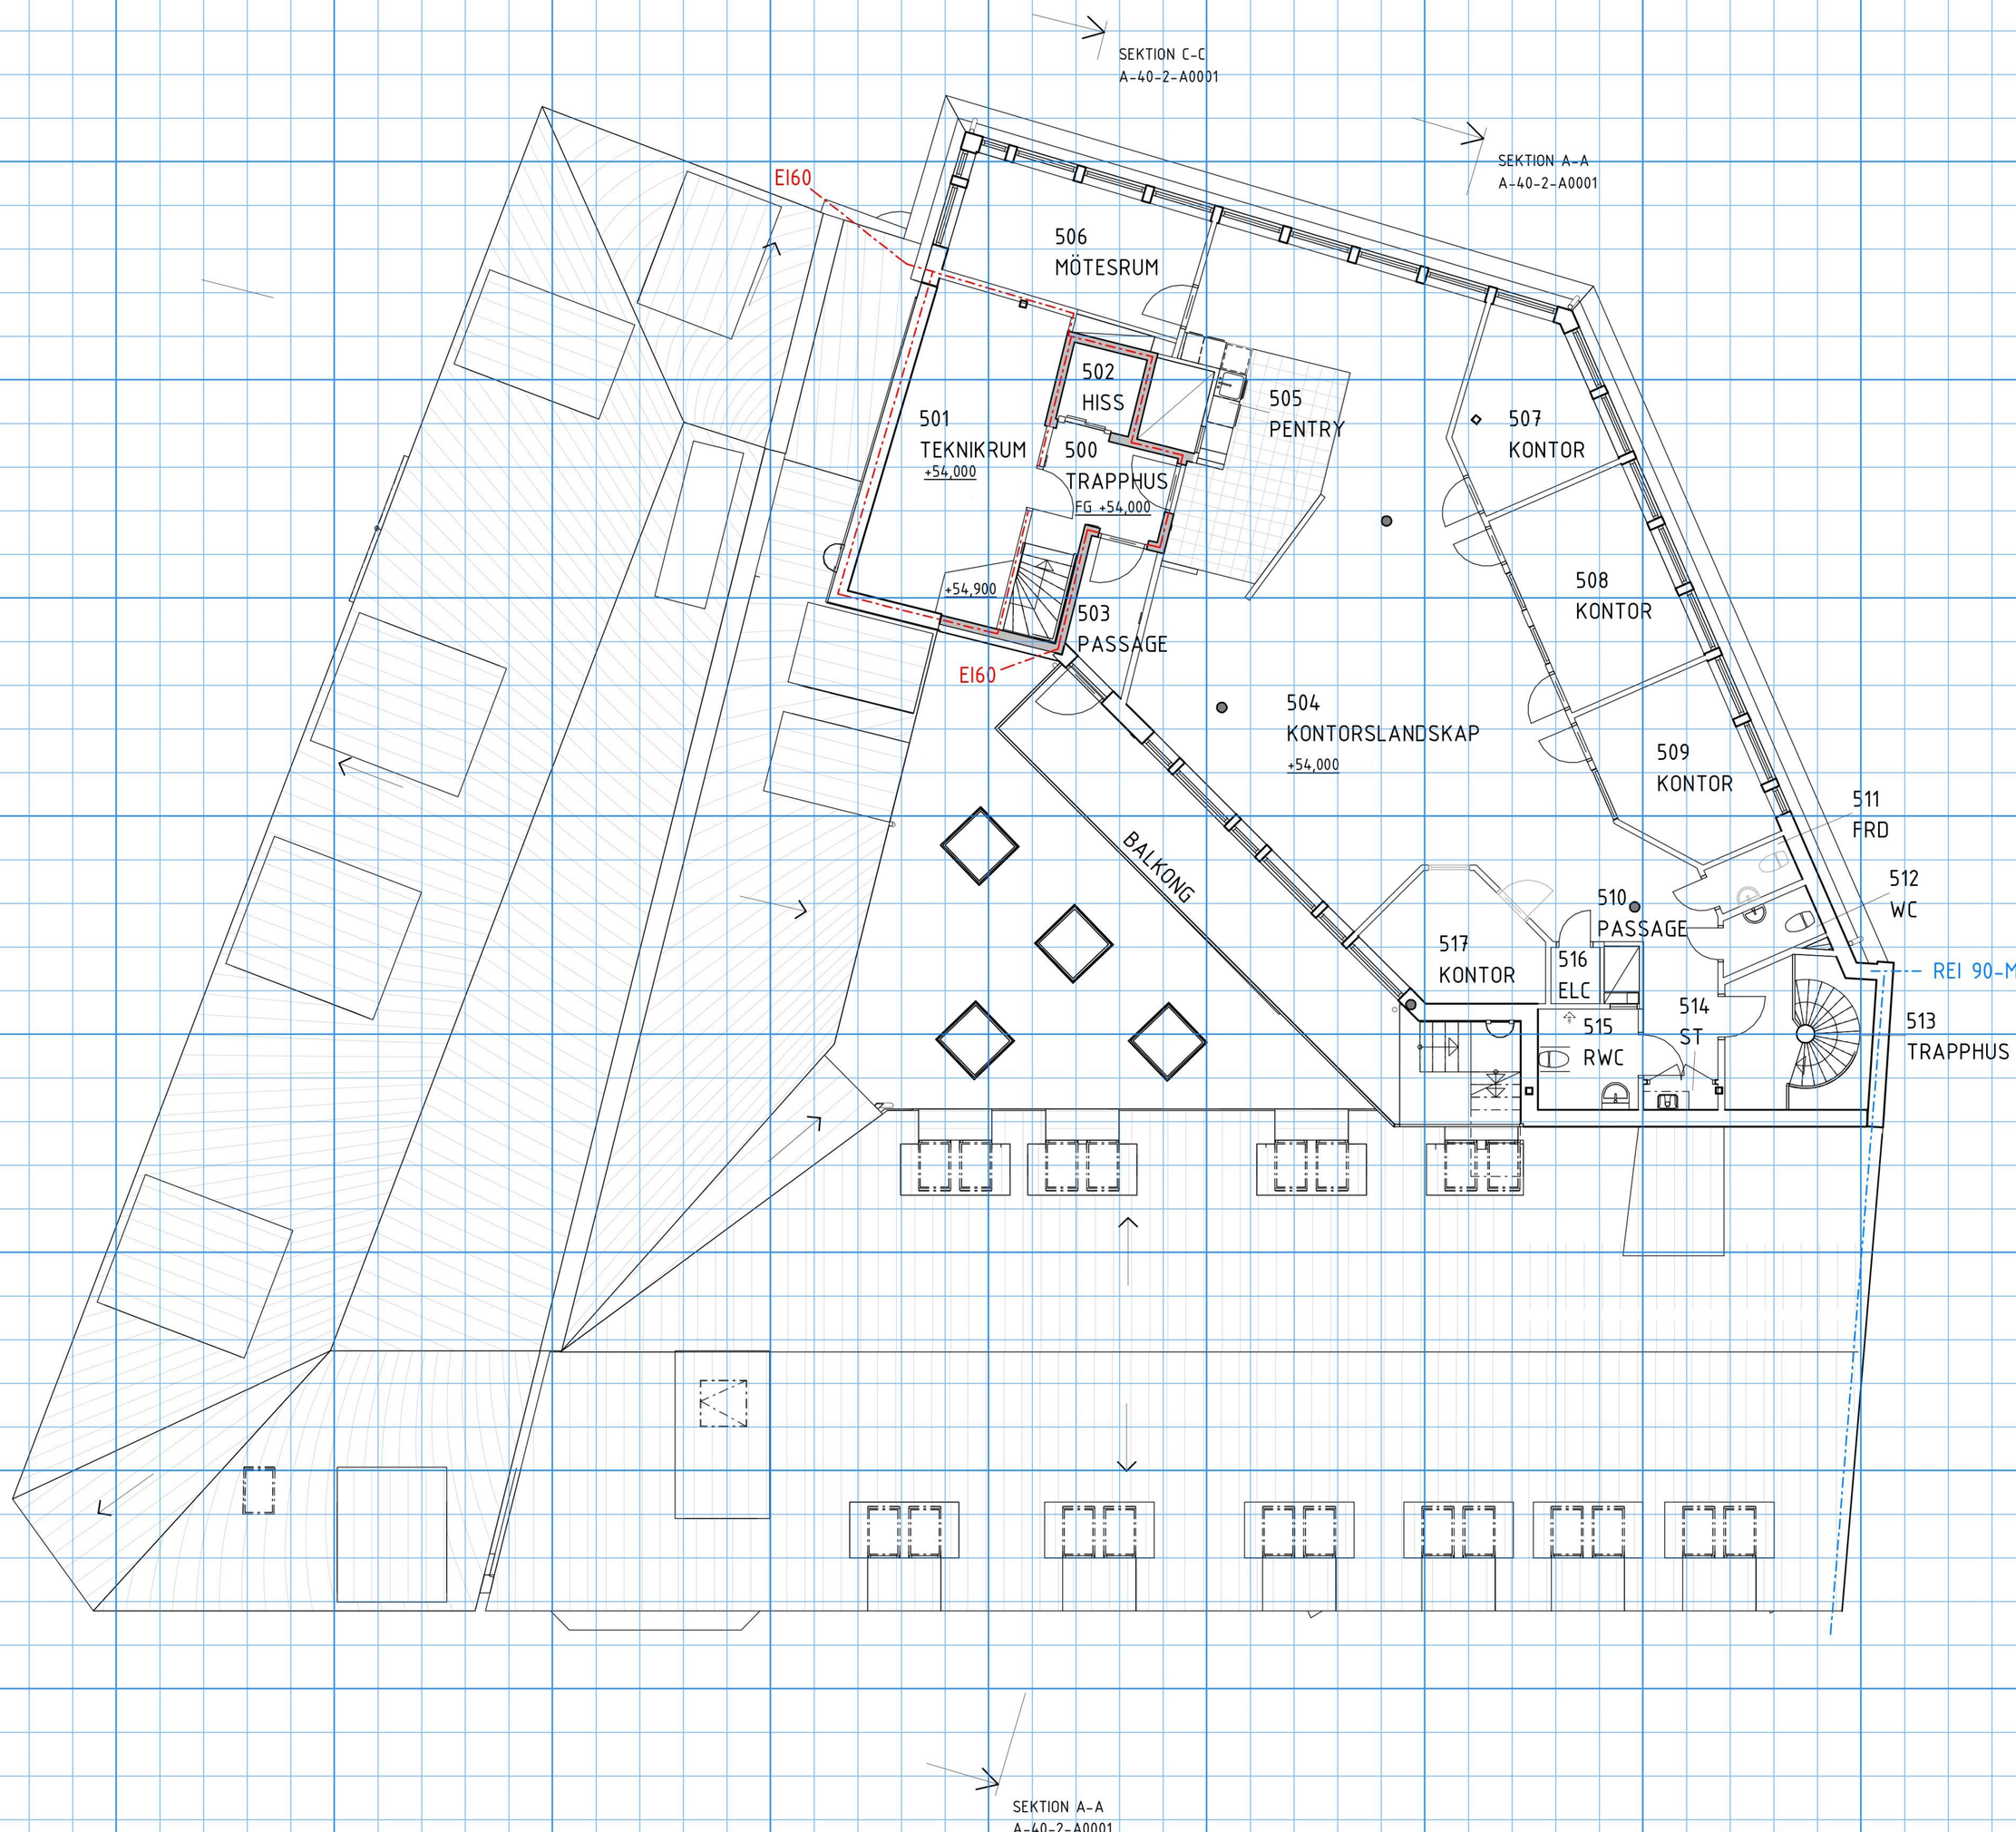
SEKTION C-C
A-40-2-A0001
SEKTION A-A
A-40-2-A0001
EI60
506
MÖTESRUM
502
HISS
505
PENTRY
501
TEKNIKRUM
+54,000
500
TRAPPHUS
FG +54,000
507
KONTOR
+54,900
503
PASSAGE
508
KONTOR
EI60
504
KONTORSLANDSKAP
+54,000
509
KONTOR
511
FRD
BALKONG
512
WC
510
PASSAGE
517
KONTOR
516
ELC
REI 90-M
514
ST
515
RWC
513
TRAPPHUS
SEKTION A-A
A-40-2-A0001